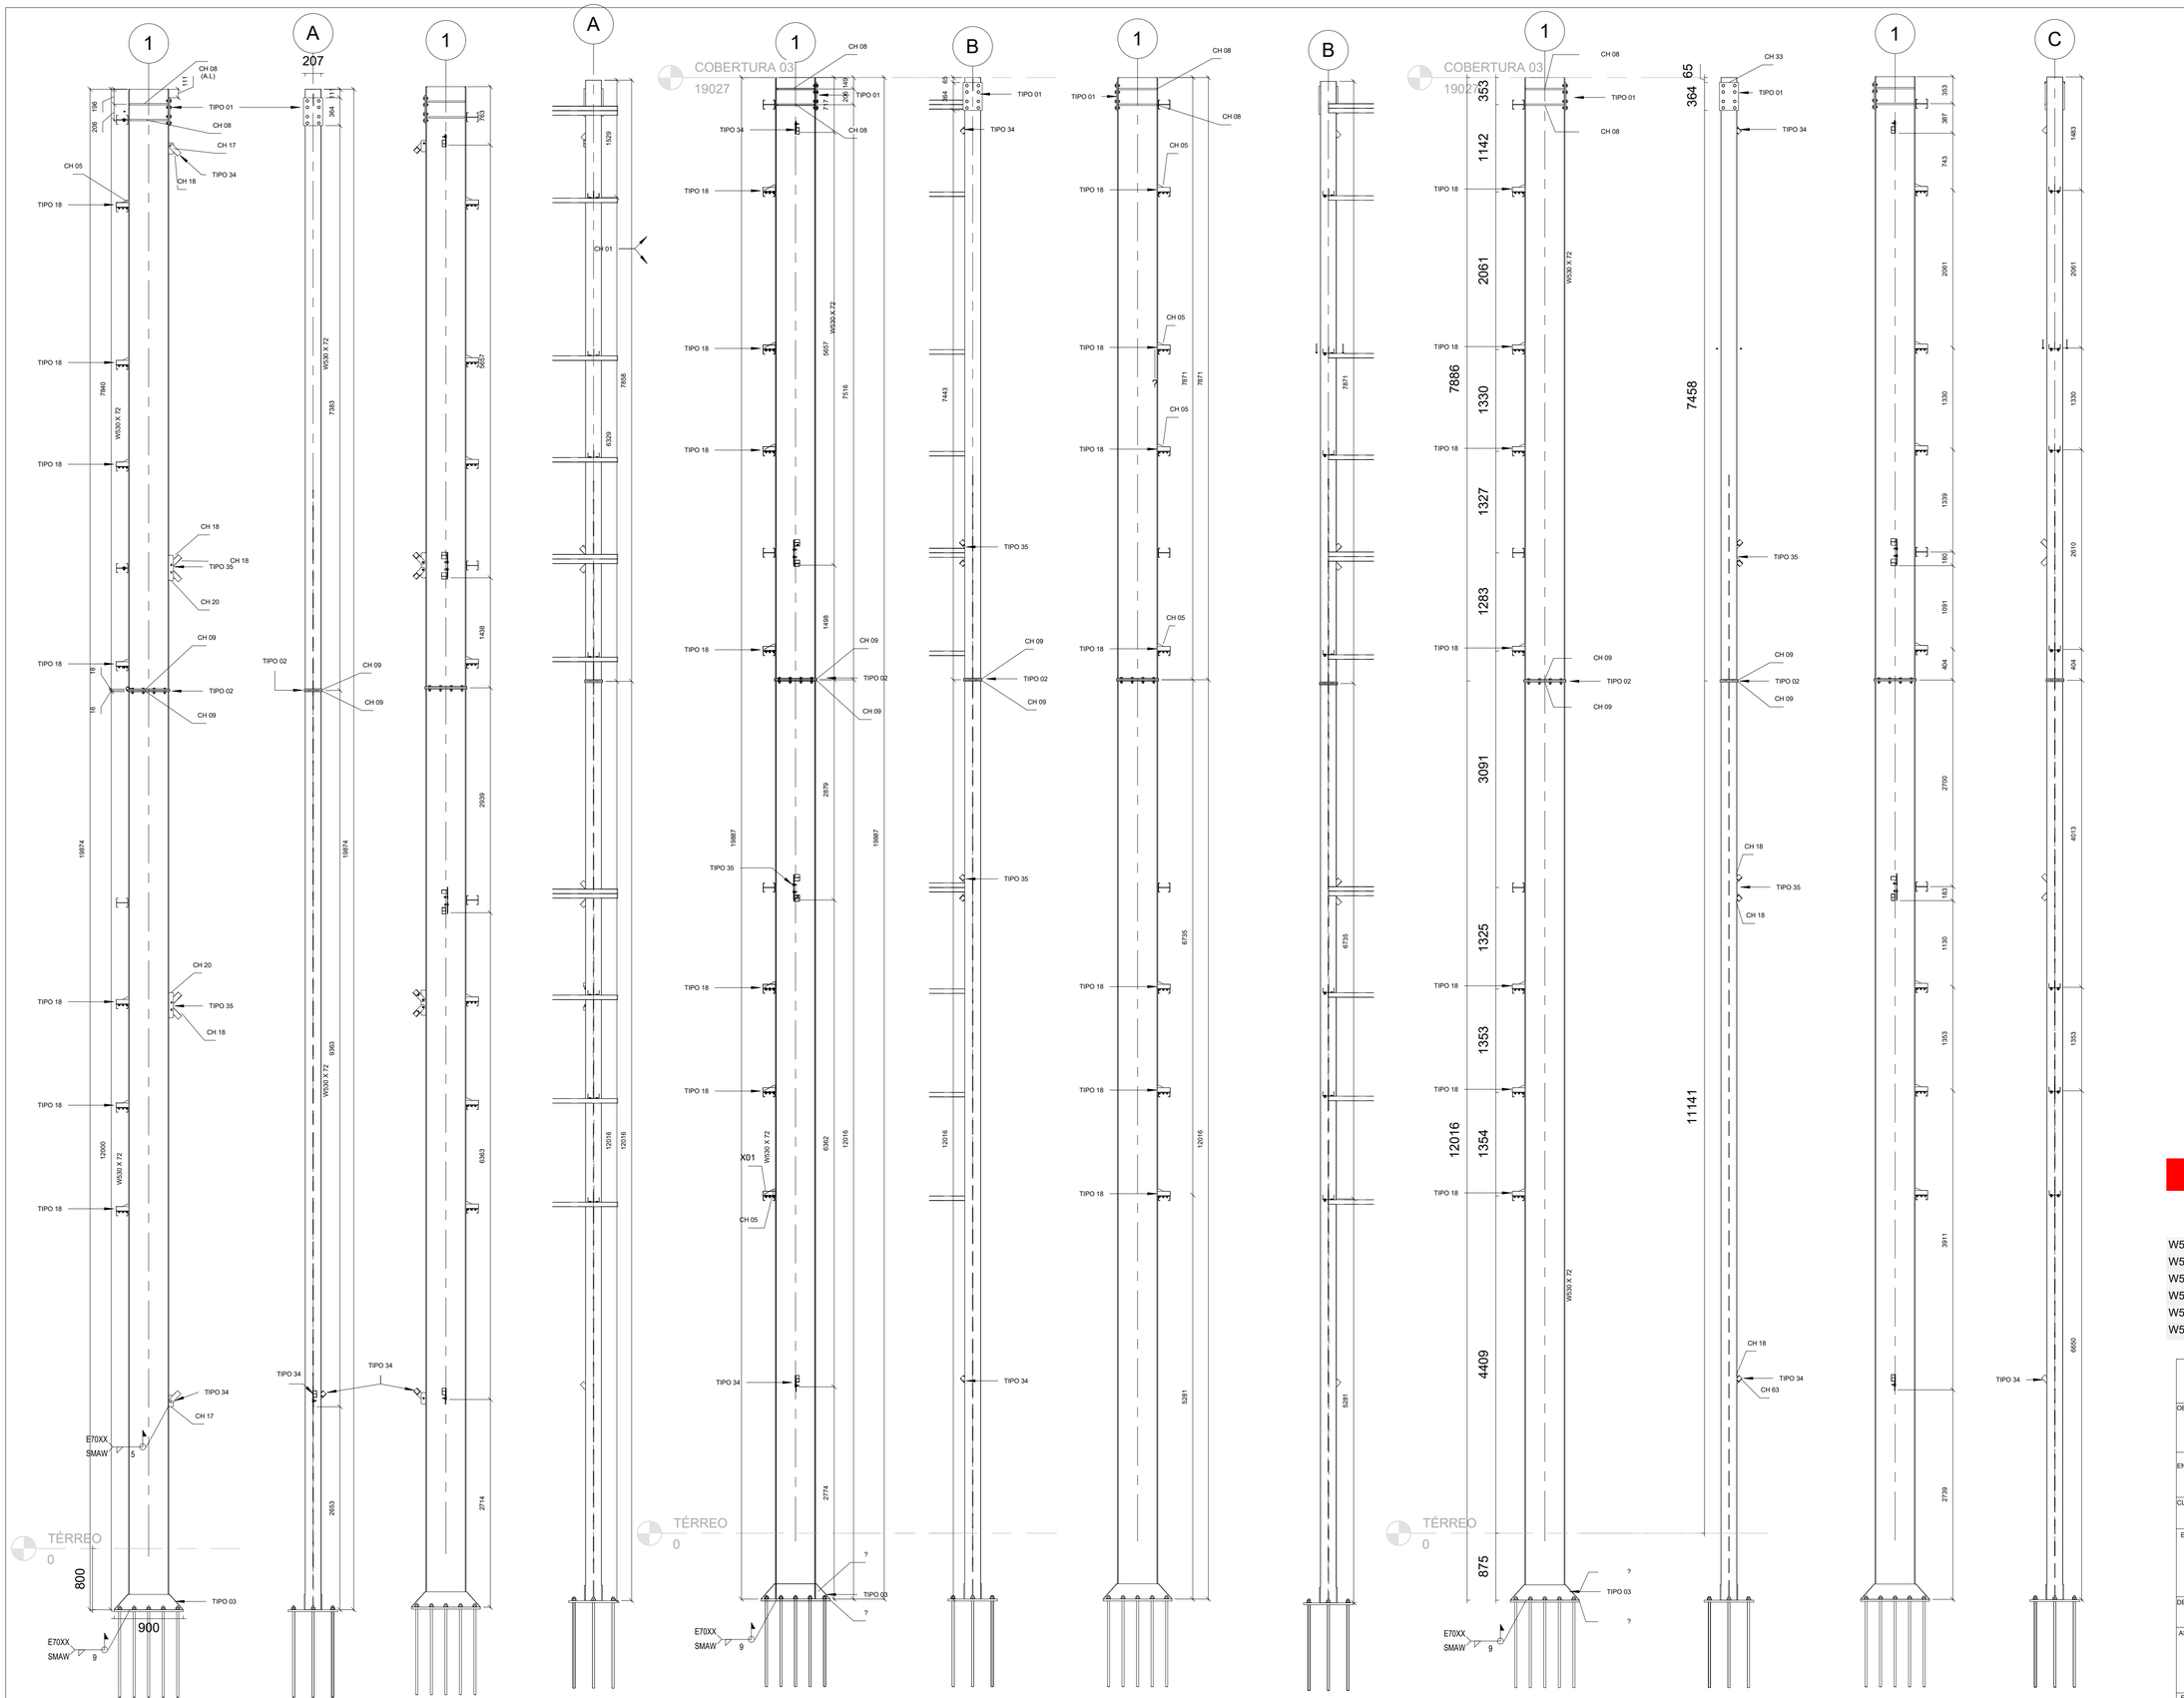

TABELA DE PERFIS - C - 01

Tipo	Comprimento do corte	Peso Total Kg	Comentários	Contagem
W530X72	7838	564.32	CO01	1
W530X72	7851	565.29	CO02	1
W530X72	7866	566.37	CO03	1
W530X72	12000	864.00	CO01	1
W530X72	12000	864.00	CO02	1
W530X72	12000	864.00	CO03	1
	59555	4287.99		

ESTRUTURA METÁLICA

OBRA/SERVIÇO :
AMPLIAÇÃO VULCAFLEX

ENDEREÇO:
UBERLÂNDIA-MG

CLIENTE:
VULCAFLEX

ENG. CIVIL	ASSINATURA:	CREA:
ALEF CHRISTIAN GOMES VIEIRA		031991896-3 AP

DESENHISTA:
ALEF CHRISTIAN GOMES VIEIRA

ASSUNTO:
DETALHAMENTO DAS COLUNAS 01 A 03

ESCALA:	DATA:	PRANCHA Nº:
INDICADO	02/11/2024	C -01

E-MAIL: engenheiroalefvieira@gmail.com