PERSPECTIVA - PLATIBANDA

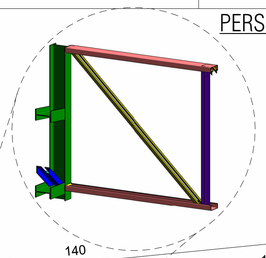

PERSPECTIVA - LIGAÇÃO BANZO SUPERIOR -TR01

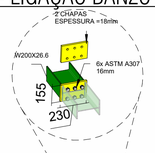

{3D} Copiar 3

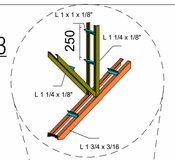

PERSPECTIVA - LIG. TERÇA - TR01

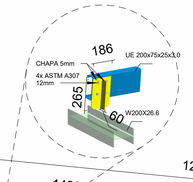

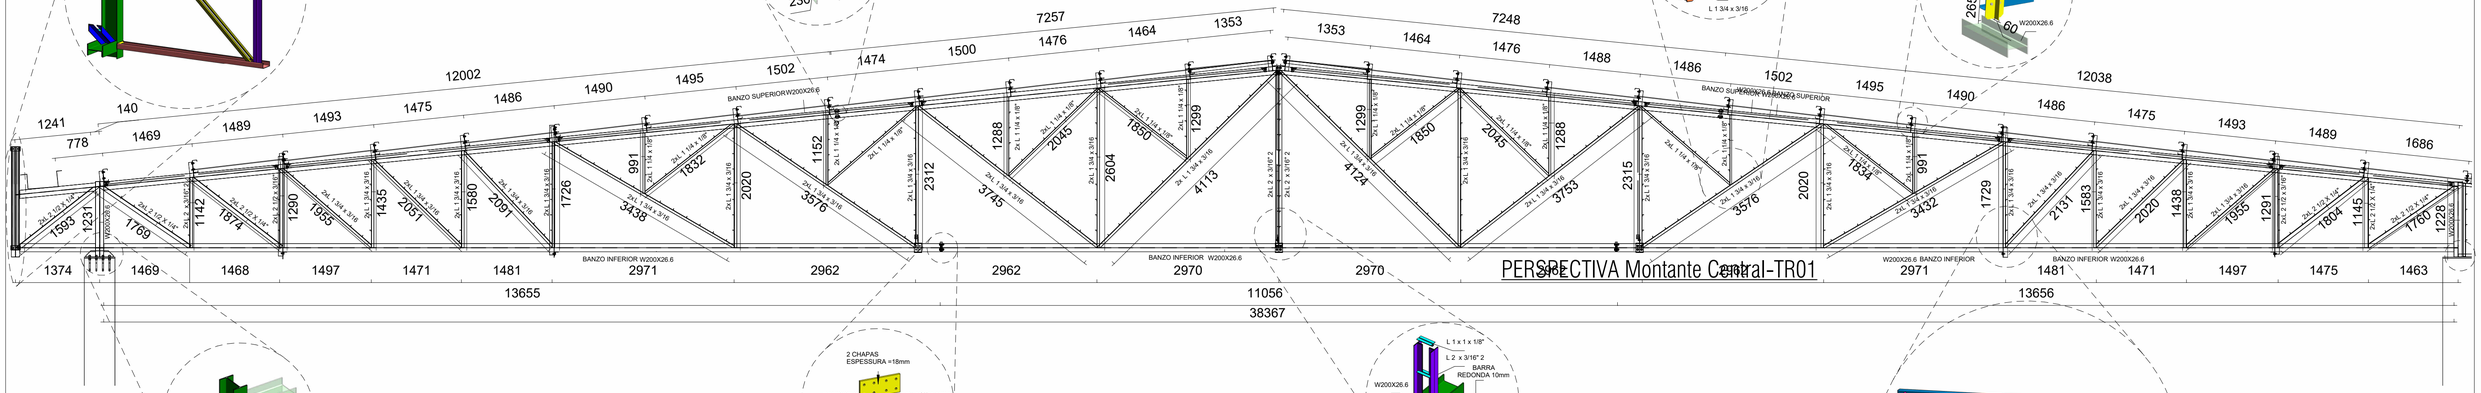

PERSPECTIVA Montante Central-TR01

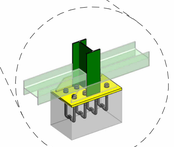

PERSPECTIVA 05 - LIG PILAR C.A 01

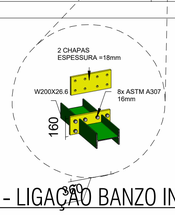

PERSPECTIVA - LIGAÇÃO BANZO INFERIOR -TR01

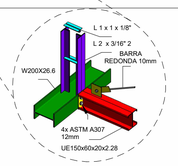

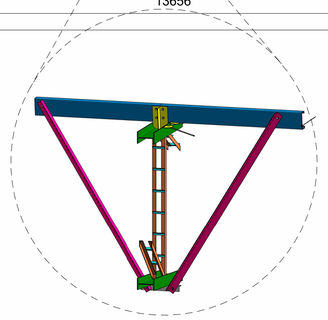

PERSPECTIVA = MÃO FRANCESA - TRELIÇA 01

Corte 1 - TRELIÇA 01

1 : 50

PERSPECTIVA - AGULHA CENTRAL

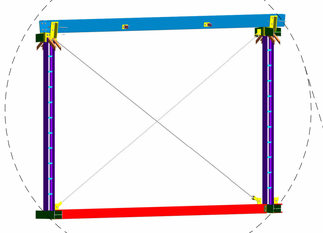

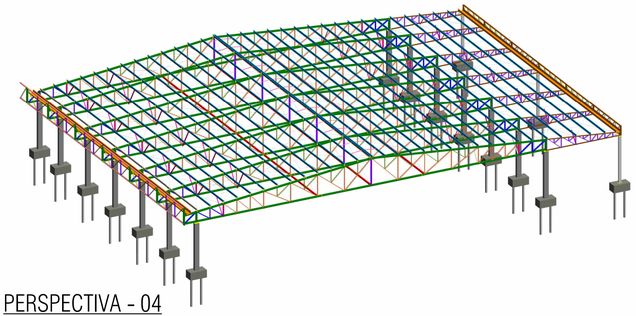

PERSPECTIVA - 04

Corte 2 - TRELIÇA 02

1 : 50

PERSPECTIVA - LIG TERÇA TR02

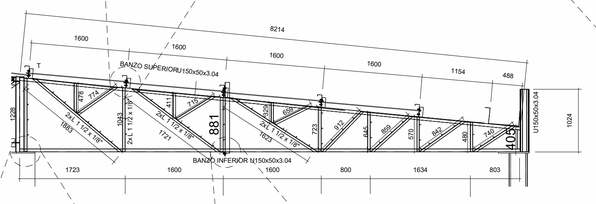

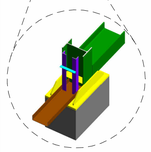

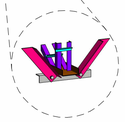

PERSPECTIVA - MÃO FRANCESA TR02

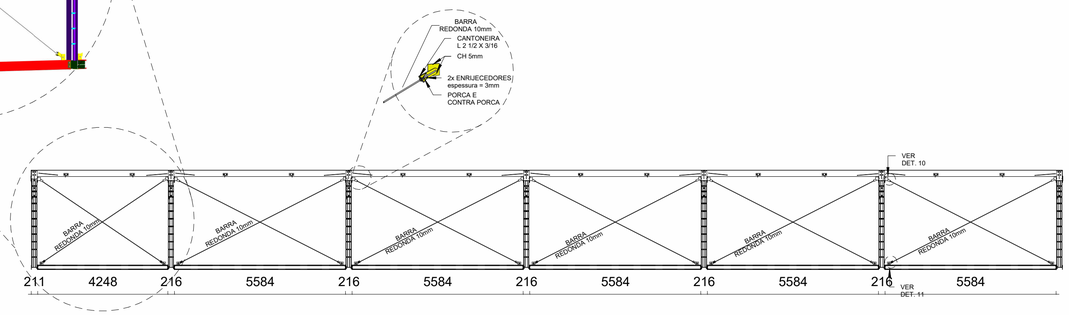

Corte 39 - AGULHAS CENTRAIS

1 : 100

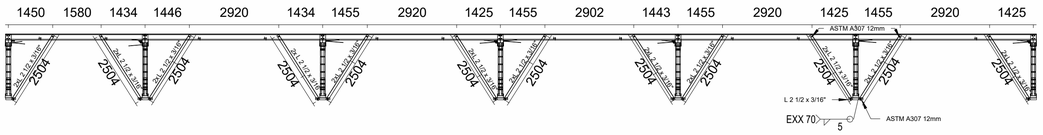

Corte 3 - MÃO FRANCESA TR01

1 : 100

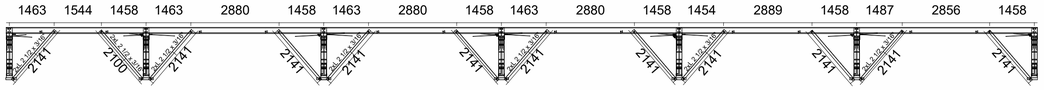

Corte 4 - MÃO FRANCESA TR01

1 : 100

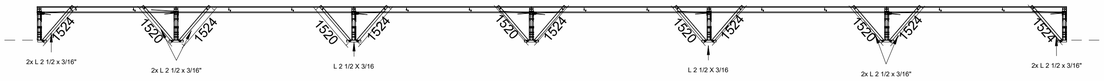

Corte 5 - MÃO FRANCESA TR02

1 : 100

PERSPECTIVA 05 - LIG PILAR C.A

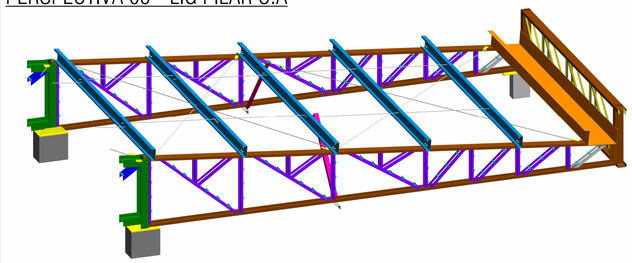

PERSPECTIVA - TRELIÇA 02

TABELA DE PERFIS METÁLICOS GERAL

Tipo	Comprimento do corte	PESO POR METRO	Peso Total Kg
BARRA REDONDA 10mm	1304.52	0.62 kg/m	808.80
L50X50X4,76	2.17	3.44 kg/m	7.46
L 1 1/2 x 1/8"	249.29	1.83 kg/m	456.20
L 1 1/4 x 1/8"	560.74	1.50 kg/m	841.11
L 1 3/4 x 3/16	987.10	1.27 kg/m	1253.61
L 1 x 1 x 1/8"	357.11	1.16 kg/m	414.24
L 2 1/2 X 1/4"	150.05	6.10 kg/m	915.29
L 2 1/2 X 3/16	16.76	4.55 kg/m	76.24
L 2 1/2 x 3/16"	160.36	1.82 kg/m	291.85
L 2 x 1/8"	32.24	2.46 kg/m	79.32
L 2 x 3/16" 2	135.02	3.63 kg/m	490.12
U150x50x3.04	213.29	6.37 kg/m	1358.63
U150x60x20x2.0	55.83	3.60 kg/m	201.00
UE150x60x20x2.28	193.23	4.11 kg/m	794.17
UE 200x75x25x3,0	1076.62	6.62 kg/m	7127.19
W200X26.6	587.26	26.60 kg/m	15621.14
	6081.57		30736.38

TABELA DE PLACAS - RESUMO

Contagem	Espessura	Peso
233	3	24.80 kg
992	5	717.62 kg
10	10	86.32 kg
77	18	474.72 kg
7	19	156.61 kg
15	20	295.22 kg
1334		1755.28 kg

TABELA DE PARAFUSOS

Diâmetro	Número
12.00 mm	1131
16.00 mm	699
	1830

ESTRUTURA METÁLICA

OBRA/SERVIÇO :

ENDEREÇO:

CLIENTE:

ENG. CIVIL | ASSINATURA: | CREA:

DESENHISTA: ALEF CHRISTIAN GOMES VIEIRA

ASSUNTO:

ESCALA: | DATA: | PRANCHA Nº:

E-MAIL: engenheiroalefvieira@gmail.com