TR - 01 (6x)

1 : 50

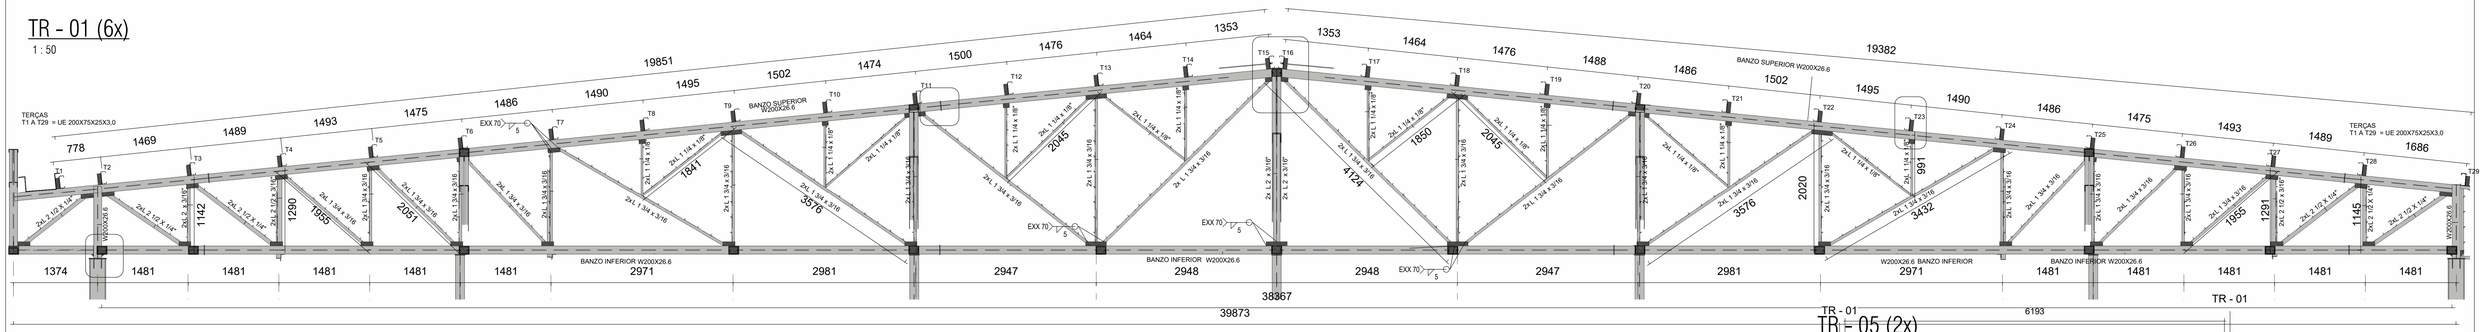

TR 02 (6X)

1 : 50

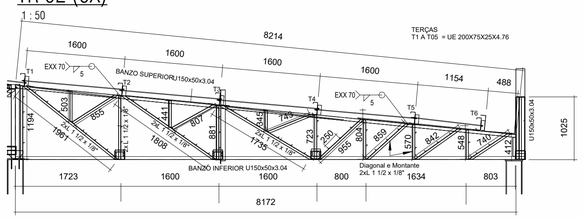

TR03 (6X)

1 : 50

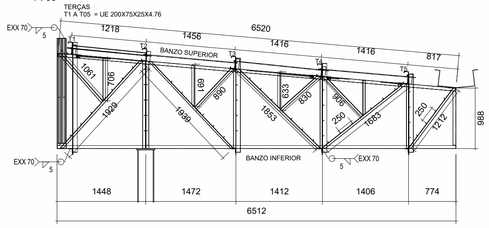

TR - 04 (2X)

1 : 50

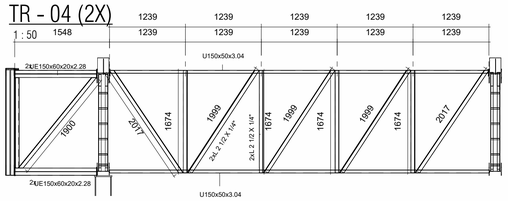

TR - 05 (2x)

1 : 50

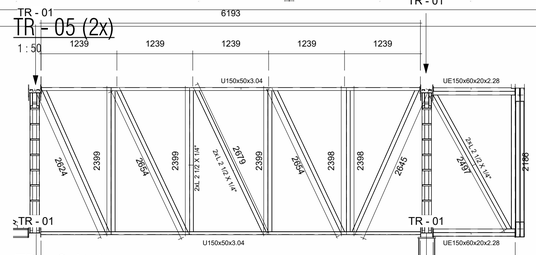

TR - 6 (1x)

1 : 50

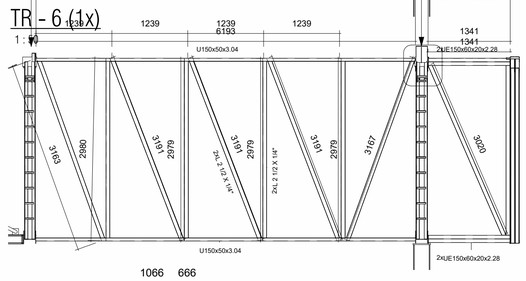

QUADRO PLATIBANDA 01 (1X)

1 : 75

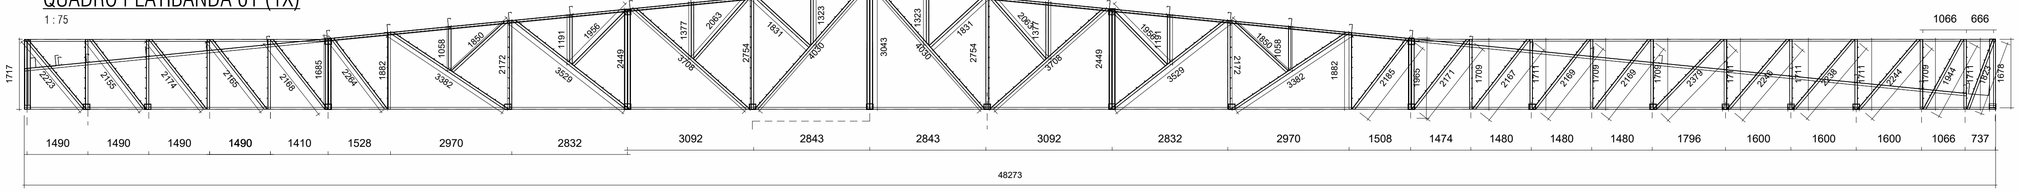

QUADRO PLATIBANDA 03

1 : 75

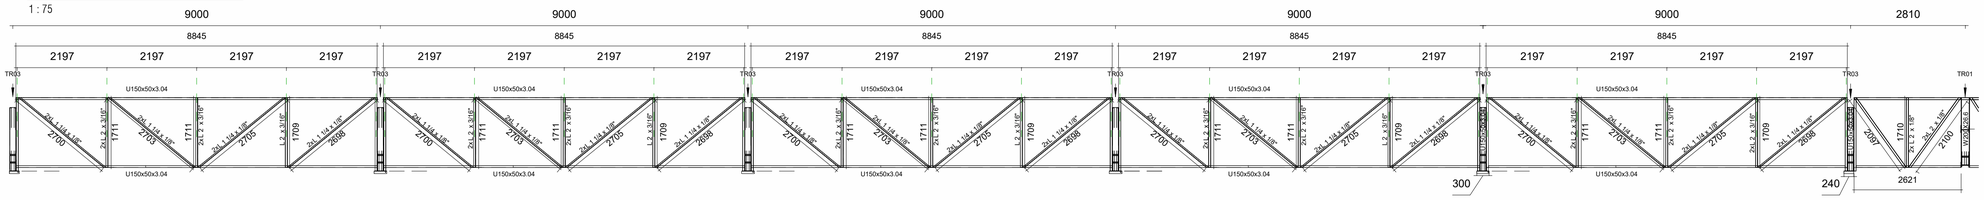

QUADRO PLATIBANDA 02 (1X)

1 : 75

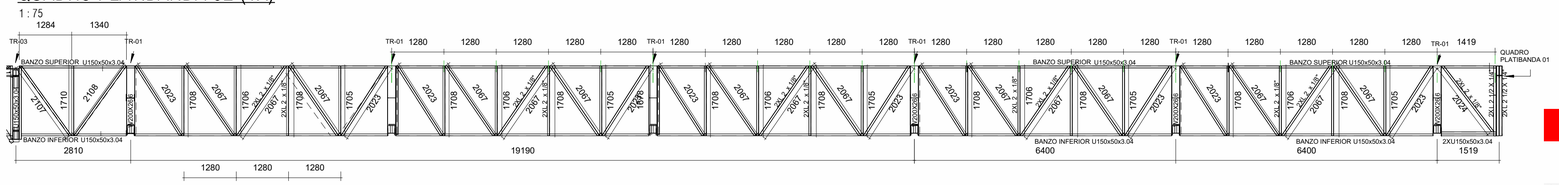

QUADRO PLATIBANDA 04

1 : 75

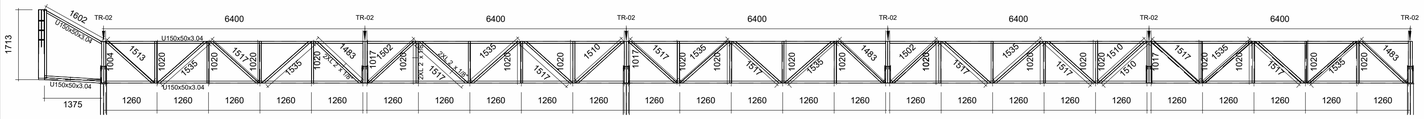

TABELA GERAL DE PERFIS METÁLICOS

Tipo	Comprimento do corte	PESO POR METRO	Peso Total Kg
BARRA REDONDA 10mm	1683.97	0.62 kg/m	1044.06
L50X50X4,76	20.32	3.44 kg/m	69.90
L 1 1/2 x 1/8"	420.29	1.83 kg/m	769.12
L 1 1/4 x 1/8"	441.17	1.50 kg/m	661.75
L 1 3/4 x 3/16	797.65	1.27 kg/m	1013.02
L 1 x 1 x 1/8"	451.24	1.16 kg/m	523.43
L 2 1/2 X 1/4"	732.40	6.10 kg/m	4467.63
L 2 1/2 X 3/16	21.71	4.55 kg/m	98.79
L 2 1/2 x 3/16"	201.85	1.82 kg/m	367.37
L 2 x 1/8"	346.81	2.46 kg/m	853.15
L 2 x 3/16"	176.35	3.63 kg/m	640.16
U150x50x3.04	620.63	6.37 kg/m	3953.42
UE150x60x20x2.28	205.27	4.11 kg/m	843.65
UE 200x75x25x3,0	1191.56	6.62 kg/m	7888.13
UE 200x75x25x4,76	225.14	6.62 kg/m	1490.43
W200X26.6	505.43	26.60 kg/m	13444.56
	8041.78		38128.56

REVISÕES

REVISÃO	NOME DA FASE			

OBSERVAÇÕES

- TODAS AS MEDIDAS DEVERÃO SER CONFERIDAS NO LOCAL.
- EM CASO DE DÚVIDA, CONSULTAR OS ARQUITETOS
- NÃO MEDIR OS DESENHOS, SEGUIR COTAS.
- EM CASO DE INCOMPATIBILIDADE, CONSULTAR OS ARQUITETOS

ENDEREÇO: Manaus -AM

Aprovador

PROPRIETÁRIO: SAMSUNG

RESPONSAVEL TÉCNICO:
RICARDO CORREA / CREA-AM 16826
Eng. Eletricista / Eng. Civil / Eng. Segurança do trabalho

CRC LTDA.

08 | 14

OBRA:
SEDA-HEAT-SAMSUNG

PROJETO
ESTRUTURA METÁLICA / CONCRETO

ETAPA:
EXECUTIVO

ENGENHEIROS:
AUTOR:
RICARDO CORREA / CREA-AM 16826
Eng. Eletricista / Eng. Civil / Eng. Segurança do trabalho
COAUTOR: Autor

CONTEUDO
ELEVAÇÃO DAS TRELIÇAS E PLATIBANDAS

ESCALA
ESC. INDIC.

DESENHO