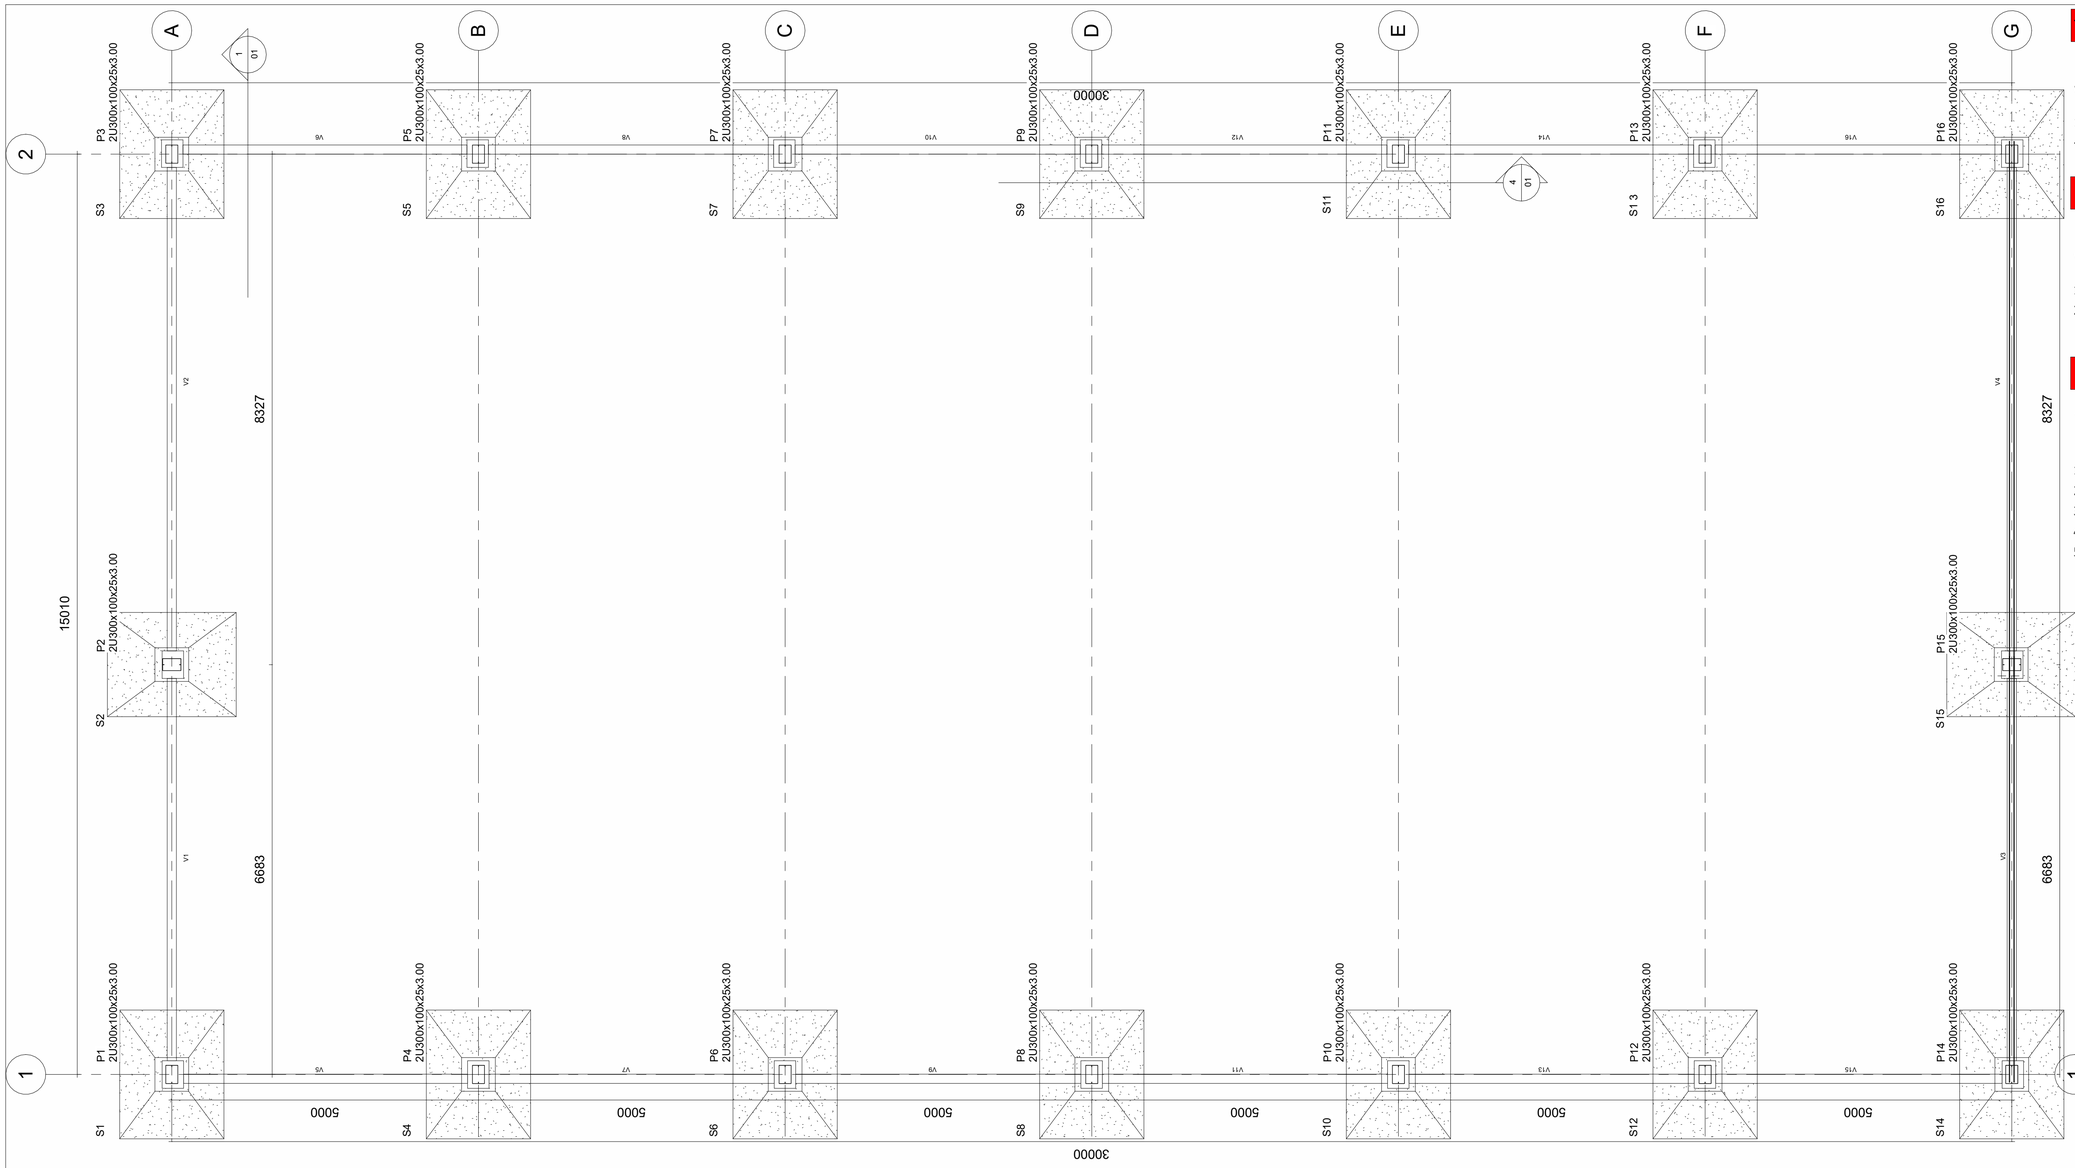

LOCAÇÃO DAS SAPATAS / PILARES

1 : 50

TABELA RESUMO DE AÇO DAS VIGAS BALDRAME...

Número do vergalhão	Diâmetro da barra	Comprimento total da barra	PESO POR METRO	PESO TOTAL
1	5.0	477.84 m	0.15 kg/m	73.59 kg
<varia>	10.0	378.92 m	0.62 kg/m	233.79 kg
		856.76 m		307.38 kg

TABELA RESUMO DE AÇO DAS SAPATAS-...

Número do vergalhão	Diâmetro da barra	Comprimento total da barra	PESO POR METRO	PESO TOTAL
1	10.0	487.78 m	0.62 kg/m	300.96 kg
2	10.0	467.57 m	0.62 kg/m	288.49 kg
		955.35 m		589.45 kg

TABELA RESUMO DE AÇO DOS PILARES-...

Número do vergalhão	Diâmetro da barra	Comprimento total da barra	PESO POR METRO	PESO TOTAL
1	10.0	41.08 m	0.62 kg/m	25.35 kg
2	10.0	41.11 m	0.62 kg/m	25.37 kg
3	5.0	415.94 m	0.15 kg/m	64.06 kg
4	10.0	32.09 m	0.62 kg/m	19.80 kg
5	10.0	31.83 m	0.62 kg/m	19.64 kg
		562.06 m		154.21 kg

NOTAS GERAIS - CONCRETO

1 : 10

1- PROJETO ESTRUTURAL DESENVOLVIDO DE ACORDO COM AS SEGUINTES NORMAS TÉCNICAS :
* NBR 6118:2019:2014 - PROJETO DE ESTRUTURAS DE CONCRETO
- PROCEDIMENTO
*NBR 6120:2019 - CARGAS PARA CÁLCULO DE ESTRUTURAS DE EDIFICAÇÕES
* * NBR 6122:2019-PROJETO E EXECUÇÃO DE FUNDAÇÕES
2- MEDIDAS EM CENTÍMETROS.
3- CARREGAMENTOS CONSIDERADOS:
3.1 - ALVENARIA DE BLOCO CERÂMICO = 1.300 kgf/m3

4- ESPECIFICAÇÃO DOS MATERIAIS:
CONCRETO:
CARACTERÍSTICA À COMPRESSÃO DE:
- SAPATAS =20MPa

5 - AS CARACTERÍSTICAS DE RESISTÊNCIA DO SOLO DEVERÃO SER CONFIRMADAS NA OBRA SOB A RESPONSABILIDADE DO CONSTRUTOR.

6-TODAS AS MEDIDAS DEVERÃO SER CONFERIDAS COM O PROJETO ARQUITETÔNICO NA OBRA. OCORRENDO DISCREPÂNCIAS ENTRE MEDIDAS, COMUNICAR COM O AUTOR DO PROJETO.
NBR 6122, E CORRELATAS. A EXECUÇÃO DAS FUNDAÇÕES IMPLICARÁ NA RESPONSABILIDADE DO CONSTRUTOR PELA RESISTÊNCIA DAS MESMAS E PELA ESTABILIDADE DA OBRA.

8-OS COBRIMENTOS DAS ARMADURAS SÃO OS SEGUINTES: 2,5cm P/ PILARES/VIGAS/LAJES E 4,0cm PARA ELEMENTOS DE FUNDAÇÃO, SENDO NECESSÁRIO O USO OBRIGATÓRIO DE ESPAÇADORES PLÁSTICOS OU
SIMILAR PARA GARANTIR OS COBRIMENTOS ESPECIFICADOS.

9-A CURA E DESFORMA DO CONCRETO DEVEM SEGUIR AS PRESCRIÇÕES DO ITEM 10 DA NBR 14931/2003-EXECUÇÃO DE ESTRUTURAS DE CONCRETO ARMADO, OBSERVANDO-SE OS
PRAZOS MÍNIMOS PARA A RETIRADA DE FÔRMAS E ESCORAMENTOS:
- FACES LATERAIS: 03 (TRÊS DIAS);
- FACES INFERIORES: DEIXANDO-SE ESCORAS APERTADAS E CONVENIENTEMENTE ESPAÇADAS: 14 DIAS
- FACES INFERIORES, SEM ESCORAMENTO: 21 DIAS
10-TODAS AS FACES EXPOSTAS DE SAPATAS, ARRANQUES DE
PILARES E CINTAS DEVERÃO RECEBER TRATAMENTO IMPERMEABILIZANTE
COM PELO MENOS 2 (DUAS) DEMÃOS DE EMULSÃO HIDROASFÁLTICA TIPO WADIMEX,
IGOL, OU SIMILAR, ANTES DO REATERRO E EXECUÇÃO DO CONTRAPISO.

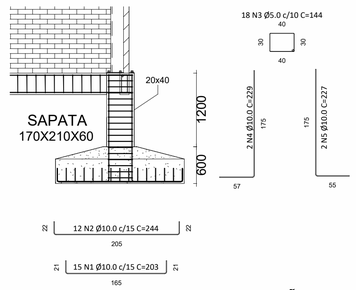

DETALHAMENTO DAS FUNDAÇÕES

1 : 50

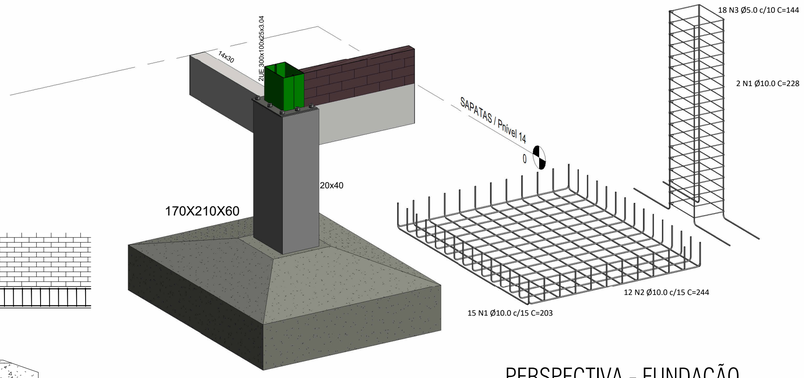

PERSPECTIVA - FUNDAÇÃO

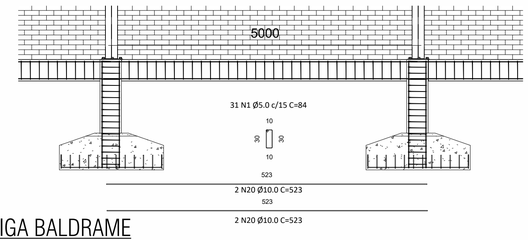

DET. VIGA BALDRAME

1 : 50

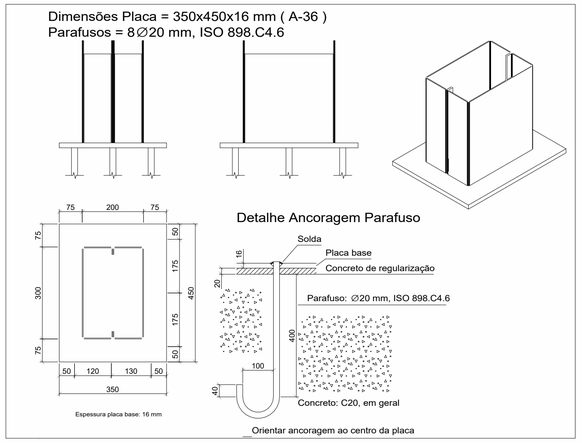

TABELA DE ÂNCORAS

Diâmetro	Comprimento	Número
20.00 mm	250	128
		128

FORMAS / CONCRETO

Tipo	Volume	Área
170X210X60	28.09 m³	57 m²
Total geral	28.09 m³	57 m²

ESTRUTURA METÁLICA

OBRA/SERVIÇO :

ENDEREÇO:

CLIENTE:

ENG. CIVIL | ASSINATURA: | CREA:

DESENHISTA:

ASSUNTO: PLANTA DE LOCAÇÃO DAS SAPATAS / PILARES ; ARMAÇÃO DAS FUNDAÇÕES /PILARES ; PERSPECTIVAS; LISTA DE MATERIAIS

ESCALA: INDICADO | DATA: 08/04/2024 | PRANCHA Nº: EST - 01

E-MAIL: engenheiroalefvieira@gmail.com