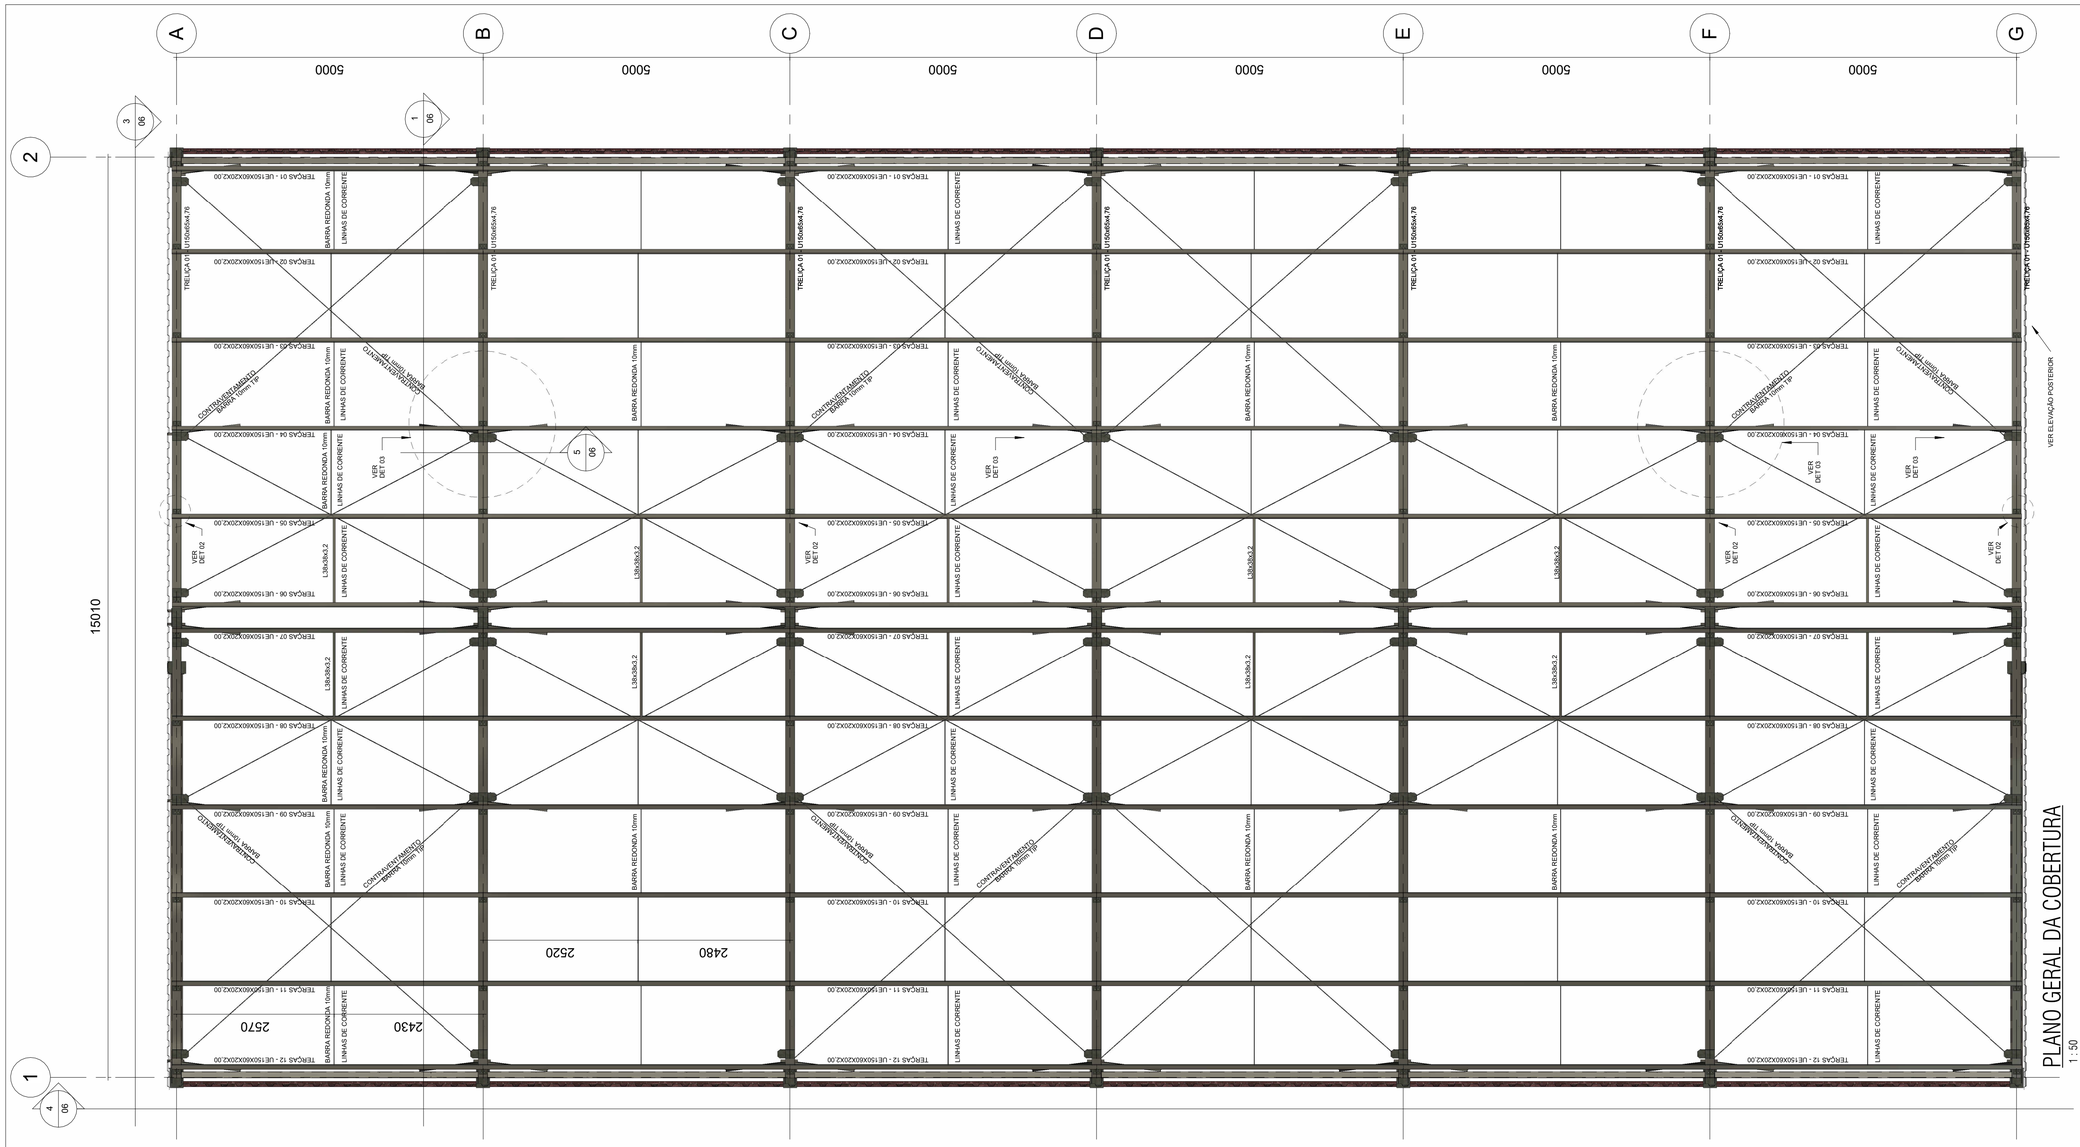


PLANO GERAL DA COBERTURA

1 : 50

## TABELA DE PERFIS METÁLICOS GERAL

| Tipo | Comprimento do corte | PESO POR METRO | Peso Total Kg |
|---|---|---|---|
| 14x30 | 84.93 | | 0.00 |
| BARRA REDONDA 10mm | 303.17 | 0.99 kg/m | 300.14 |
| L38x38x3,2 | 701.94 | 1.42 kg/m | 996.76 |
| L100X100X3,0 | 10.08 | | 0.00 |
| L100X100X6.3 | 4.40 | 1.71 kg/m | 7.53 |
| u75x38x4,47 | 24.56 | | 0.00 |
| U75x40x15x1.90 | 99.29 | | 0.00 |
| U100x50x3.04 | 116.09 | | 0.00 |
| U150x60x20x2.0 | 361.90 | | 0.00 |
| U150x65x4.76 | 211.64 | | 0.00 |
| U200x75x20x2.00 | 25.66 | 5.91 kg/m | 151.66 |
| UE 300x100x25x3.04 | 194.73 | | 0.00 |
| | 2138.40 | | 1456.10 |

## TELHA METÁLICA

| Tipo | Material: Área |
|---|---|
| PERFIL METÁLICO | 186 m² |
| Telha Metálica - Trapezoidal | 1356 m² |
| | 1542 m² |

## TABELA DE PLACAS

| Contagem | Espessura | Largura | Comprimento | Peso |
|---|---|---|---|---|
| 439 | 3 | 50 | 125 | 64.62 kg |
| 62 | 3 | 66 | 133 | 6.84 kg |
| 7 | 3 | 80 | 620 | 8.72 kg |
| 7 | 3 | 80 | 621 | 8.74 kg |
| 14 | 3 | 93 | 300 | 8.87 kg |
| 14 | 3 | 142 | 300 | 13.22 kg |
| 28 | 3 | 150 | 170 | 17.94 kg |
| 24 | 5 | 120 | 150 | 16.28 kg |
| 22 | 5 | 140 | 280 | 31.50 kg |
| 20 | 5 | 140 | 441 | 44.75 kg |
| 78 | 10 | 50 | 120 | 36.74 kg |
| 28 | 10 | 117 | 221 | 39.75 kg |
| 4 | 10 | 200 | 250 | 15.70 kg |
| 2 | 10 | 200 | 300 | 9.42 kg |
| 16 | 10 | 350 | 450 | 197.82 kg |
| 14 | 16 | 220 | 320 | 123.79 kg |
| 779 | | | | 644.69 kg |

## NOTAS GERAIS - METÁLICA

1 : 10

1- DIMENSÕES EM MILÍMETRO, EXCETO ONDE INDICADO DE OUTRA FORMA.
2 - ELETRODOS E60XX PARA ELEMENTOS ESTRUTURAIS EXCETOPARA AS PLACAS DE BASE, ONDE VAI OS CHUMBADORES QUE É E70XX. OBSERVAR COMPATIBILIDADE DO ELETRODO COM O MATERIAL A SOLDAR.
3 - FAZER PRE-MONTAGEM EM TODAS PEÇAS DA ESTRUTURA METÁLICA
4 - SOLDAS
4.1 ALTURA DO FILETE IGUAL A DA CHAPA MAIS FINA;
4.2 SOLDAR AS PEÇAS EM TODO CONTORNO DE CONTATO;
4.3 PARA SOLDA ELÉTRICA RETIFICADORA USAR AMPERAGEM<160A;
4.4 ESPECIFICAÇÕES DE SOLDAS: VER DETALHES.
5 - PERFIS LAMINADOS TIPO CANTONEIRA E CHAPAS PLANAS GROSSAS: AÇO ASTM A36, fy 250 MPa.
6 - PERFIS EM CHAPA DOBRADA TIPO: ASTM A36, MR250 (fy = 250 MPa).
7 - CHUMBADORES DO TIPO CAL DE AÇO A36 (ROSCA GALVANIZADA)
8 - NORMAS UTILIZADAS NESTE PROJETO
- NBR-8800 (2008) - PROJETO E EXECUÇÃO DE ESTRUTURAS DE AÇO DE EDIFÍCIOS;
- NBR-14.762 (2001) - DIMENSIONAMENTO DE ESTRUTURAS DE AÇO CONSTITUIDAS POR PERFIS FORMADOS A FRIO
- NBR-6120 (2019) - CARGAS PARA O CÁLCULO DE ESTRUTURAS DE EDIFICAÇÕES;
- NBR-6123 (1988) - FORÇAS DEVIDAS AO VENTO EM EDIFICAÇÕES;
- NBR-8681 (2003) - AÇÕES E SEGURANÇA NAS ESTRUTURAS;
9 - PINTURA: A ESPECIFICAÇÃO DE PINTURA DA ESTRUTURA METÁLICA TERÁ SUA SUPERFÍCIE PREPARADA E JATEADA ATÉ ATINGIR METAL QUASE BRANCO.
A PINTURA TERÁ :
- UMA PRIMEIRA DEMÃO COM FUNDO EPÓXI MARTIC COM 100 MICRAS;
- UMA SEGUNDA DEMÃO COM FUNDO EPÓXI MARTIC COM 100 MICRAS;
- UMA TERCEIRA DEMÃO COM TINTA DE ACABAMENTO POLIURETANO ALIFÁTICO 40 MICRAS.
10 - PARAFUSOS DE ALTA RESISTÊNCIA ASTM-A307 GALVANIZADOS

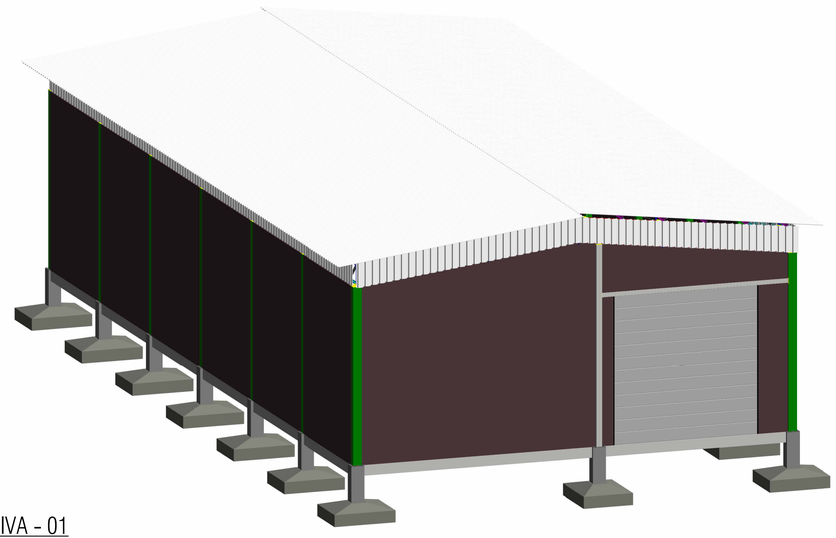

PERSPECTIVA - 01

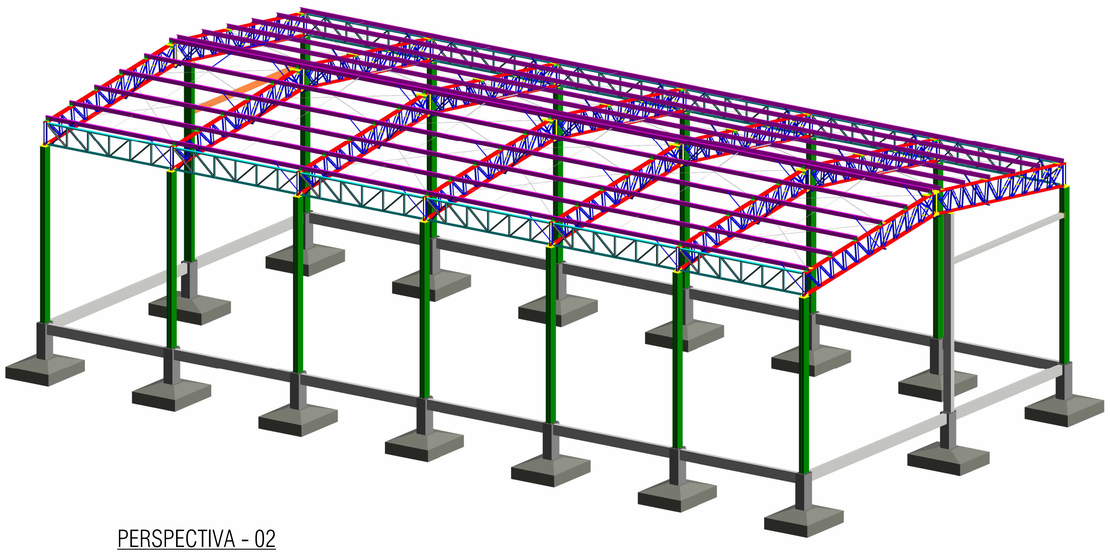

PERSPECTIVA - 02

## ESTRUTURA METÁLICA

OBRA/SERVIÇO :

ENDEREÇO:

CLIENTE:

| ENG. CIVIL | ASSINATURA: | CREA: |
|---|---|---|
| | | |

DESENHISTA:

ASSUNTO:

| ESCALA: | DATA: | PRANCHA Nº: |
|---|---|---|
| | | |

E-MAIL: engenheiroalefvieira@gmail.com