ELEVAÇÃO MÃO FRANCESA
1 : 25

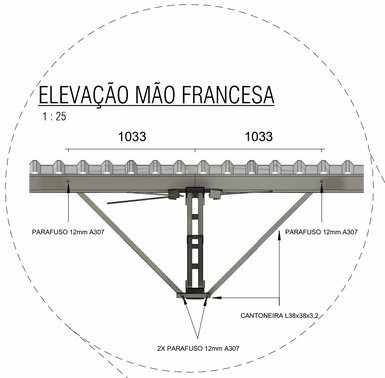

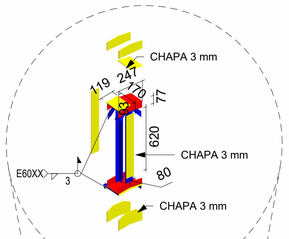

PERSPECTIVA - 03

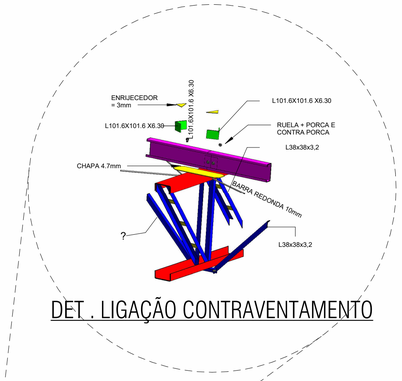

DET . LIGAÇÃO CONTRAVENTAMENTO

TABELA DE PERFIS METÁLICOS GERAL

Tipo	Comprimento do corte	PESO POR METRO	Peso Total Kg
14x30	84.93		0.00
BARRA REDONDA 10mm	303.17	0.99 kg/m	300.14
L38x38x3,2	695.03	1.42 kg/m	986.95
L101.6X101.6 X6.30	4.40	10.01 kg/m	44.09
L101.6x101.6 x 3,2	10.08	5.00 kg/m	50.40
u75x38x4,47	24.56	5.20 kg/m	127.73
U75x40x15x1.90	99.29	2.70 kg/m	268.08
U100x50x3.04	116.09	4.53 kg/m	525.88
U150x60x20x2.0	361.90	4.66 kg/m	1686.45
U150x65x4.76	211.64	9.87 kg/m	2088.87
U200x75x20x2.00	25.66	5.91 kg/m	151.66
UE 300x100x25x3.04	194.73	25.28 kg/m	4922.70
	2131.49		11152.94

TABELA DE PARAFUSOS

Diâmetro	Número
12.00 mm	136
	336
	472

ELEVAÇÃO DA TRELIÇA (7X)
1 : 25

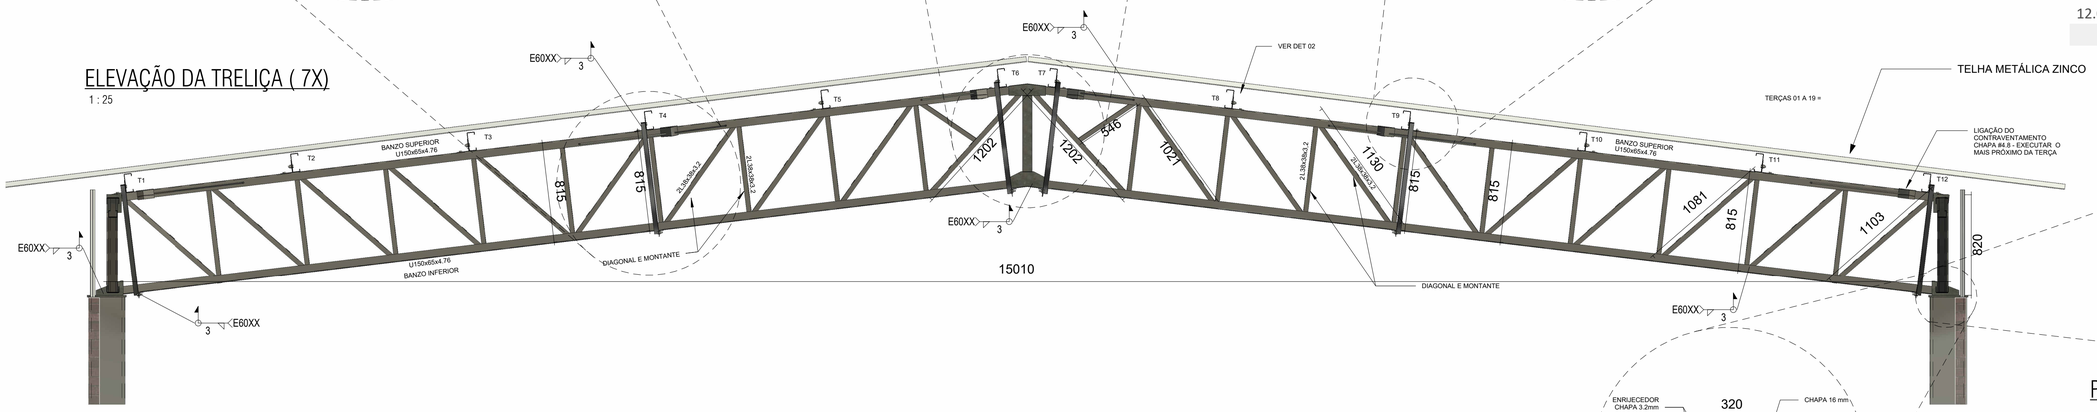

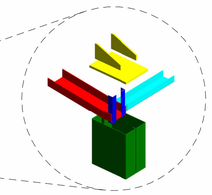

PERSPECTIVA - 05 - TOPO PILAR (16X)

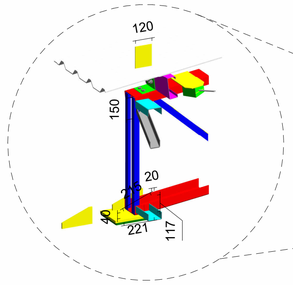

TRELIÇA TIPO 2 (12X)
1 : 25

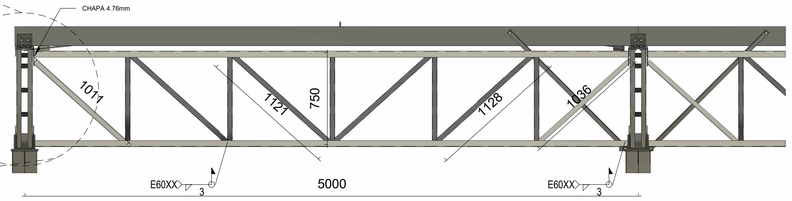

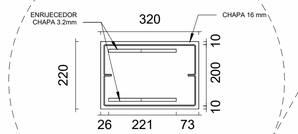

CHAPA TOPO PILAR
1 : 10

NOTAS GERAIS - METÁLICA
1 : 10

1- DIMENSÕES EM MILÍMETRO, EXCETO ONDE INDICADO DE OUTRA FORMA.
2 - ELETRODOS E60XX PARA ELEMENTOS ESTRUTURAIS EXCETOPARA AS PLACAS DE BASE, ONDE VAI OS CHUMBADORES QUE É E70XX . OBSERVAR COMPATIBILIDADE DO ELETRODO COM O MATERIAL A SOLDAR.
3 - FAZER PRÉ-MONTAGEM EM TODAS PEÇAS DA ESTRUTURA METÁLICA
4 - SOLDAS
4.1 ALTURA DO FILETE IGUAL A DA CHAPA MAIS FINA;
4.2 SOLDAR AS PEÇAS EM TODO CONTORNO DE CONTATO;
4.3 PARA SOLDA ELÉTRICA RETIFICADORA USAR AMPERAGEM<160A;
4.4 ESPECIFICAÇÕES DE SOLDAS: VER DETALHES.
5 - PERFIS LAMINADOS TIPO CANTONEIRA E CHAPAS PLANAS GROSSAS: AÇO ASTM A36, fy 250 MPa.
6 - PERFIS EM CHAPA DOBRADA TIPO: ASTM A36, MR250 (fy = 250 MPa).
7 - CHUMBADORES DO TIPO CAL DE AÇO A36 (ROSCA GALVANIZADA)
8 - NORMAS UTILIZADAS NESTE PROJETO
- NBR-8800 (2008) - PROJETO E EXECUÇÃO DE ESTRUTURAS DE AÇO DE EDIFÍCIOS;
- NBR-14.762 (2001) - DIMENSIONAMENTO DE ESTRUTURAS DE AÇO CONSTITUIDAS POR PERFIS FORMADOS A FRIO
- NBR-6120 (2019) - CARGAS PARA O CÁLCULO DE ESTRUTURAS DE EDIFICAÇÕES;
- NBR-6123 (1988) - FORÇAS DEVIDAS AO VENTO EM EDIFICAÇÕES;
- NBR-8681 (2003) - AÇÕES E SEGURANÇA NAS ESTRUTURAS;
9 - PINTURA: A ESPECIFICAÇÃO DE PINTURA DA ESTRUTURA METÁLICA TERÁ SUA SUPERFÍCIE PREPARADA E JATEADA ATÉ ATINGIR METAL QUASE BRANCO.
A PINTURA TERÁ :
- UMA PRIMEIRA DEMÃO COM FUNDO EPÓXI MARTIC COM 100 MICRAS;
- UMA SEGUNDA DEMÃO COM FUNDO EPÓXI MARTIC COM 100 MICRAS;
- UMA TERCEIRA DEMÃO COM TINTA DE ACABAMENTO POLIURETANO ALIFÁTICO 40 MICRAS.
10 - PARAFUSOS DE ALTA RESISTÊNCIA ASTM-A307 GALVANIZADOS

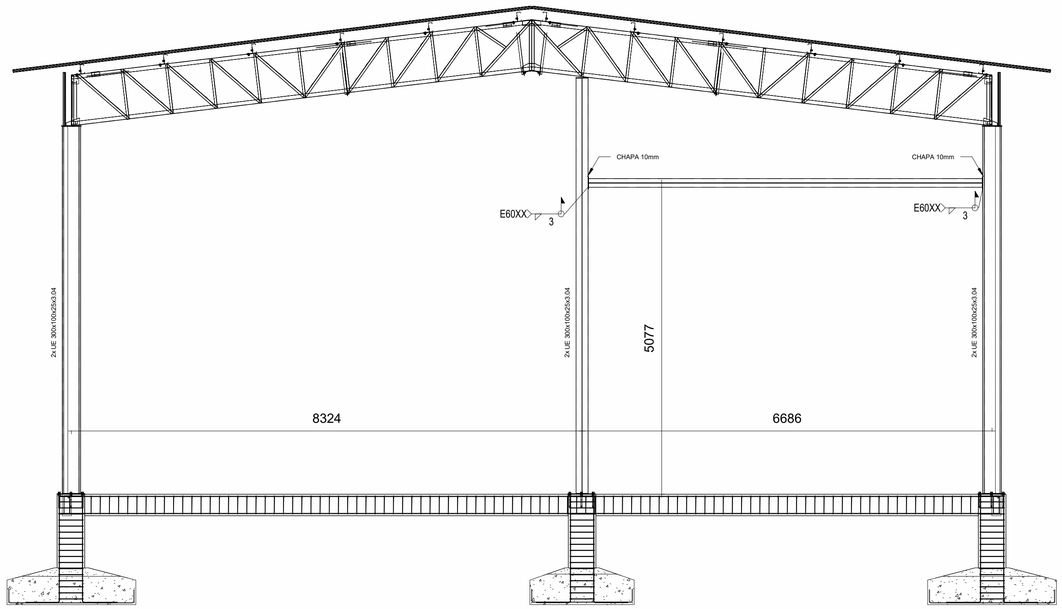

ELEVAÇÃO FRONTAL / POSTERIOR
1 : 50

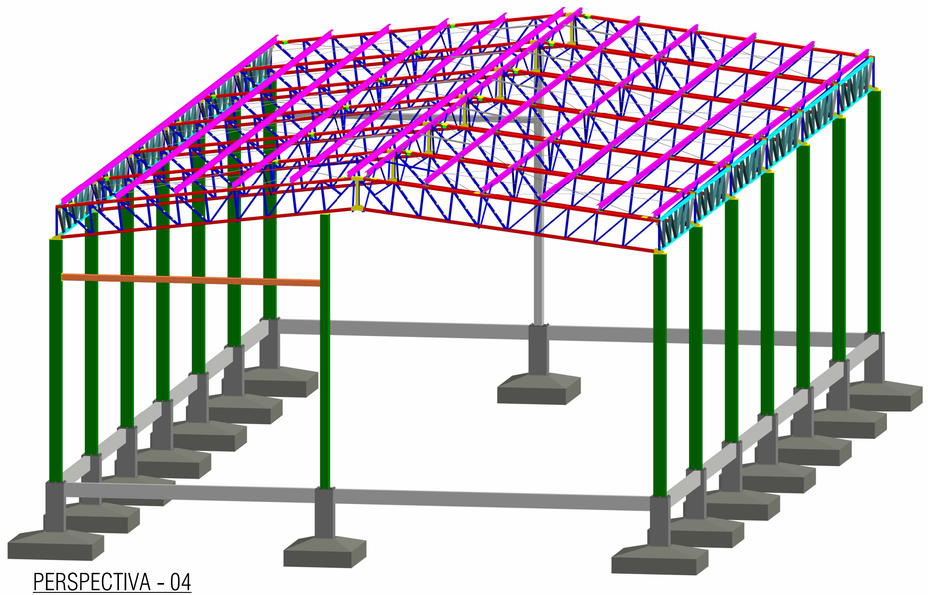

PERSPECTIVA - 04

ESTRUTURA METÁLICA

OBRA/SERVIÇO :

ENDEREÇO:

CLIENTE:

ENG. CIVIL	ASSINATURA:	CREA:

DESENHISTA: ALEF CHRISTIAN GOMES VIEIRA

ASSUNTO: DETALHAMENTO DAS TRELIÇAS ; ELEVAÇÕES ; PERSPECITAS ; LISTA DE MATERIAIS

ESCALA:	DATA:	PRANCHA Nº:
INDICADO		EST - 03

E-MAIL: engenheiroalefvieira@gmail.com